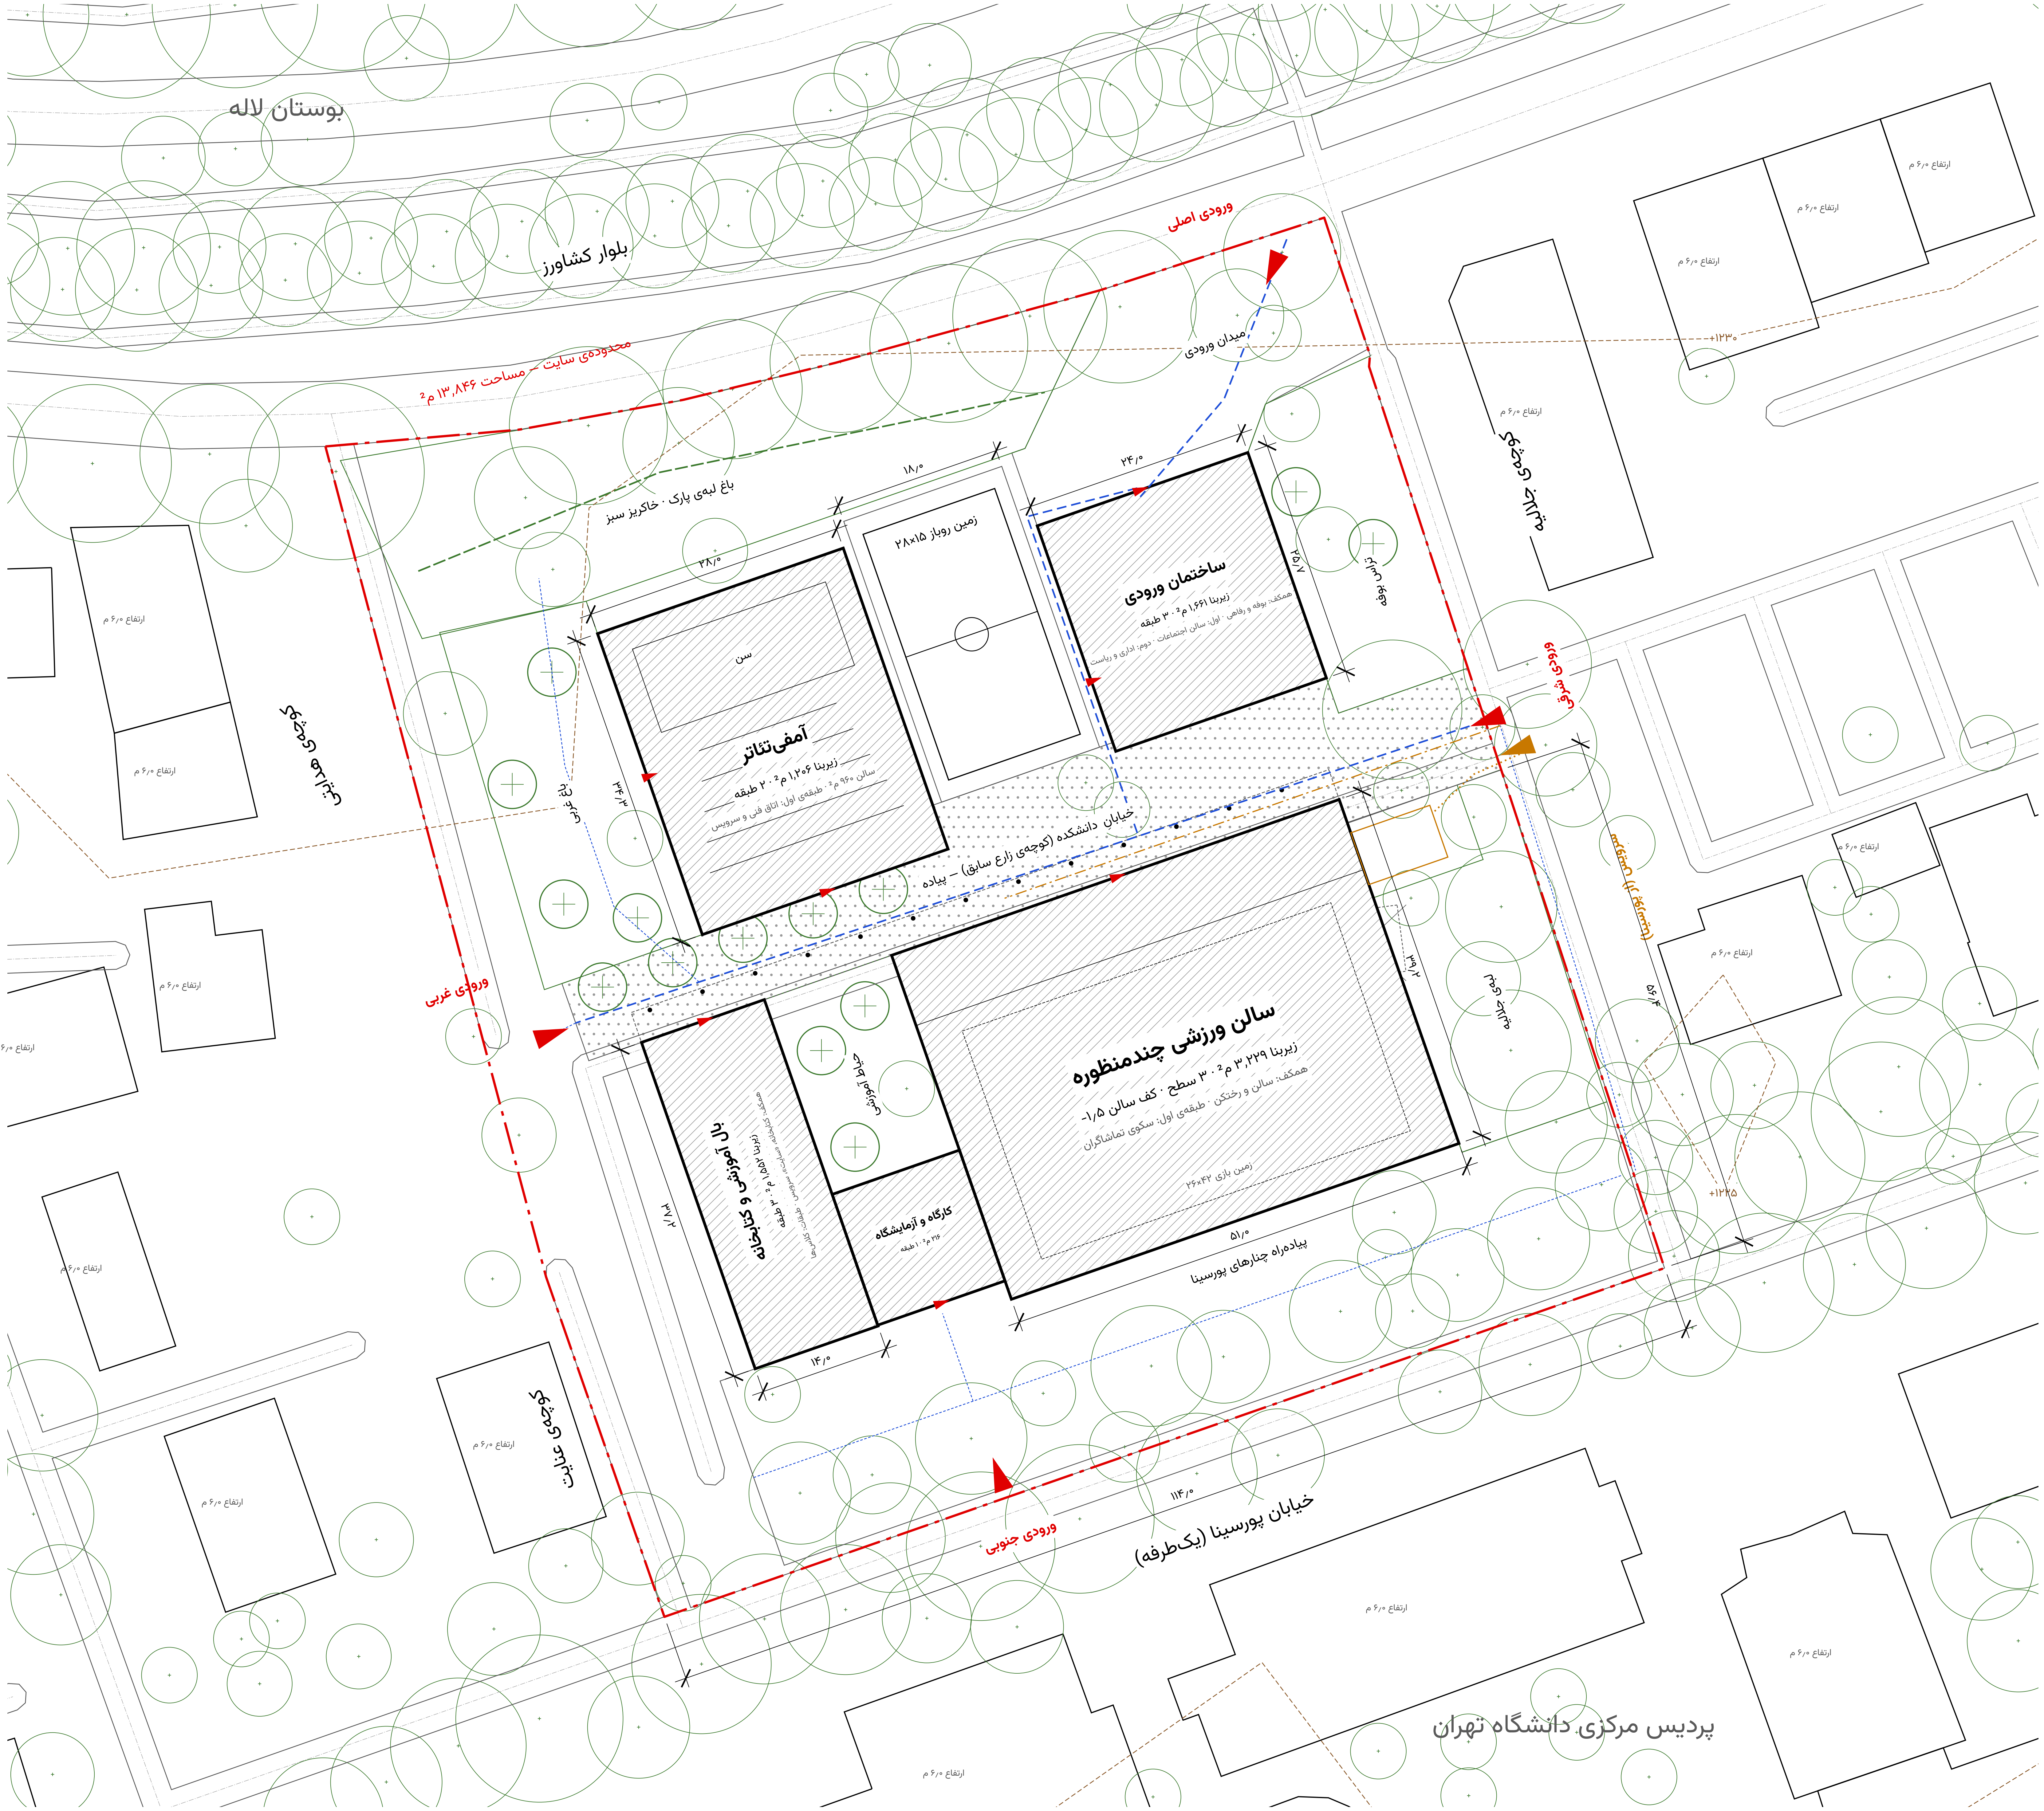
بوستان لاله
بلوار کشاورز
محدوده‌ی سایت – مساحت ۱۳,۸۴۶ م²
ورودی اصلی
میدان ورودی
باغ لبه‌ی پارک · خاکریز سبز
۱۸/۰
۲۴/۰
۲۸/۰
زمین روباز ۲۸×۱۵
ساختمان ورودی
زیربنا ۱,۶۶۱ م² · ۳ طبقه
همکف: بوفه و رفاهی · اول: سالن اجتماعات · دوم: اداری و ریاست
۷/۵۸
تراس بوفه
کوچه‌ی جلالیه
ورودی شرقی
سرویس (از پورسینا)
لبه‌ی جلالیه
۴/۶۵
۲/۶۳
سن
آمفی‌تئاتر
زیربنا ۱,۲۰۶ م² · ۲ طبقه
سالن ۹۶۰ م² · طبقه‌ی اول: اتاق فنی و سرویس
۳/۴۳
باغ غربی
کوچه‌ی هدایت
ورودی غربی
خیابانِ دانشکده (کوچه‌ی زارع سابق) – پیاده
سالن ورزشی چندمنظوره
زیربنا ۳,۲۲۹ م² · ۳ سطح · کف سالن ۱/۵-
همکف: سالن و رختکن · طبقه‌ی اول: سکوی تماشاگران
زمین بازی ۴۲×۲۶
۵۱/۰
پیاده‌راه چنارهای پورسینا
بال آموزشی و کتابخانه
زیربنا ۱,۵۸۲ م² · ۳ طبقه
همکف: کتابخانه، «سایت»، سرویس · طبقات: کلاس‌ها
حیاط آموزشی
کارگاه و آزمایشگاه
۲۱۶ م² · ۱ طبقه
۱۴/۰
۳۷/۸۲
۱۱۴/۰
کوچه‌ی عنایت
ورودی جنوبی
خیابان پورسینا (یک‌طرفه)
پردیس مرکزی دانشگاه تهران
ارتفاع ۶/۰ م
+۱۲۳۰
+۱۲۲۵

مقیاس ۱:۵۰۰

واحد: متر · روی کاغذ A2

۰ ۵ ۱۰ ۱۵ ۲۰ ۲۵

شمال

راهنما

▨	ساختمان پیشنهادی (هاشور)
—	ساختمان موجود
— · —	محدوده‌ی سایت
– – –	مسیر اصلی پیاده
······	مسیر فرعی پیاده
— · —	دسترسی اضطراری
······	سرویس و بارگیری
– – –	خط تراز ۵ متری
⊕	درخت پیشنهادی
○	درخت موجود
▶	ورودی
☒	بنای موجود – تخریب

جدول مساحت‌ها (متر مربع)

فضا	خالص	ناخالص	ساختمان
کلاس‌های تئوری	۸۲۰	۱,۱۹۴	آموزشی
سالن ورزشی چندمنظوره	۲,۳۹۲	۳,۲۲۹	سالن
آمفی‌تئاتر	۸۵۵	۱,۱۵۴	آمفی
کتابخانه	۱۶۱	۲۱۷	آموزشی
سالن اجتماعات	۳۸۱	۵۱۲	ورودی
کارگاه و آزمایشگاه	۱۶۰	۲۱۶	کارگاه
سایت (کاربری نامشخص)	۶۶	۸۹	آموزشی
اتاق‌های اداری	۱۸۴	۲۴۹	ورودی
ریاست و معاونت‌ها	۲۵۱	۳۴۰	ورودی
فضای تفریحی / رفاهی	۱۱۶	۱۶۰	ورودی
بوفه	۲۵۸	۳۴۸	ورودی
سرویس‌های بهداشتی	۱۱۵	۱۵۶	۳ ساختمان
جمع	**۵,۷۵۹**	**۷,۸۶۴**	

مساحت سایت: ۱۳,۸۴۵ م²
سطح اشغال: ۴,۳۱۳ م² (۳۱٪)
تعداد طبقات: ۱ تا ۳

یادداشت‌ها

۱. نقشه‌ی پایه همان فایل DXF سایت است و تغییری نکرده.
۲. محدوده روی لبه‌ی خیابان‌های بلوک ترسیم شده (غیرثبتی).
۳. کاربری فضای «سایت» در برنامه مشخص نیست.
۴. تراز دقیق زمین نیاز به نقشه‌برداری دارد.

طراحی دانشکده‌ی تربیت بدنی دانشگاه تهران

عنوان نقشه: سایت‌پلان ایده – «خیابانِ دانشکده»

موقعیت: تهران، منطقه‌ی ۶ – میان بوستان لاله و دانشگاه تهران

دانشجو:	استاد:	مقیاس: **۱:۵۰۰**
تاریخ: **۱۴۰۵/۰۷/۲۲**	مرحله: **ایده**	شماره‌ی شیت: **۱ از ۱**